
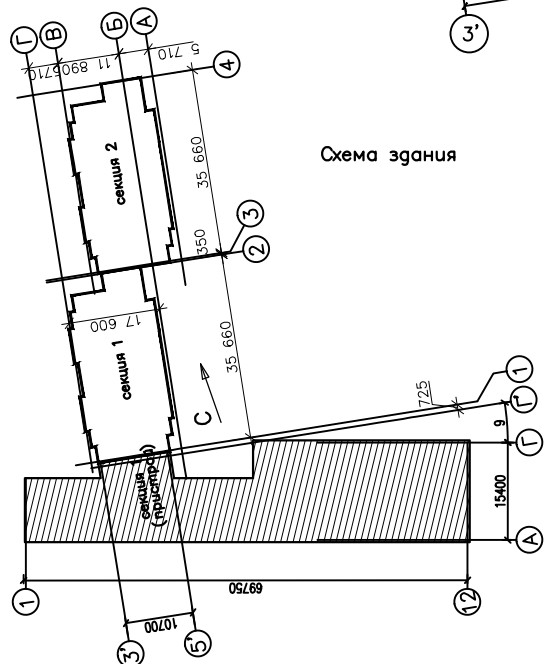


План 1-го этажа

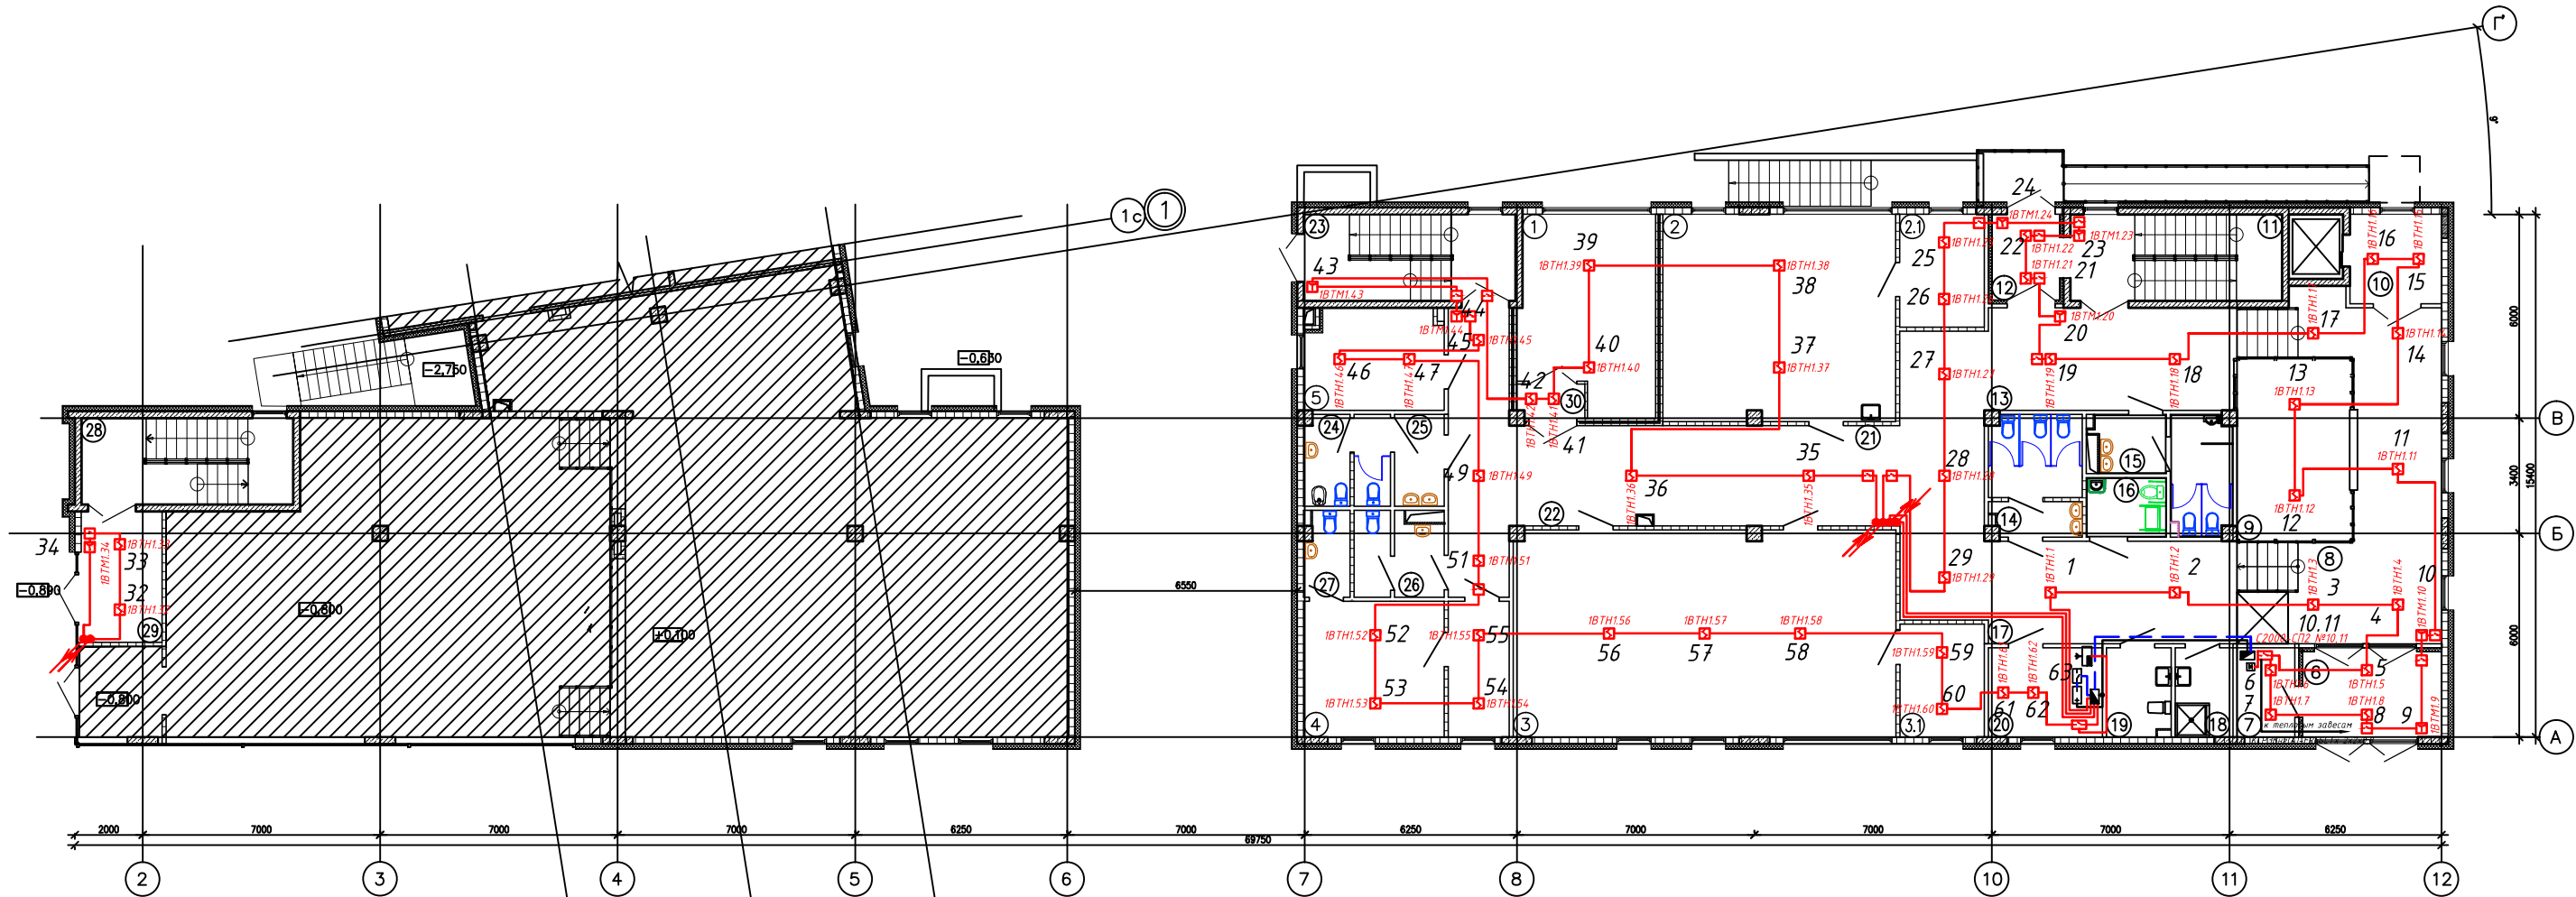

ЭКСПЛИКАЦИЯ ПОМЕЩЕНИЙ (начало)

| Номер помеще-ния | Наименование | Площадь м2 | Катег. помеще-ния |
|--|--|------------|-------------------|
| 1 этаж Художественное отделение-группа раннего музыкального развития | | | |
| 1 | Класс групповых занятий (группа раннего музыкального развития) 3-5 лет. 10 чел. | 21,53 | |
| 2 | Класс групповых занятий (живопись, рисунок) 10 чел. | 41,29 | |
| 2.1 | Помещение для хранения экспонатов | 8,05 | |
| 3 | Класс групповых занятий (прикладного искусства, композиции и анимации). 15 чел. | 67,96 | |
| 3.1 | Помещение для хранения экспонатов | 8,05 | |
| 4 | Административный кабинет (руководителя). 15 чел. | 11,65 | |
| 5 | Административный кабинет (учебная часть) | 11,65 | |
| 6 | Тамбур главного входа | 10,73 | |
| 7 | Охрана | 4,31 | |
| 8 | Вестибюль с зоной ожидания для родителей | 36,39 | |
| 9 | Гардероб | 17,61 | |
| 10 | Лифтовой тамбур | 7,13 | |
| 11 | Лестничная клетка | 15,56 | |
| 12 | Тамбур | 5,08 | |
| 13 | Коридор | 22,00 | |

ЭКСПЛИКАЦИЯ ПОМЕЩЕНИЙ (окончание)

| Номер помеще-ния | Наименование | Площадь м2 | Катег. помеще-ния |
|--|--|------------|-------------------|
| 1 этаж Художественное отделение-группа раннего музыкального развития | | | |
| 14 | С/узел "Ж" | 9,01 | |
| 15 | С/узел "М" | 9,56 | |
| 16 | С/узел для "МП" | 4,00 | |
| 17 | Коридор | 21,84 | |
| 18 | Помещение уборочного инвентаря | 4,32 | В 4 |
| 19 | С/узел для посетителей | 4,73 | |
| 20 | Электрощитовая | 8,64 | |
| 21 | Коридор | 32,85 | В 3 |
| 22 | Коридор | 35,98 | |
| 23 | Лестничная клетка | 15,56 | |
| 24 | Комната личной гигиены (КЛГ) | 3,44 | |
| 25 | С/у "Ж" | 6,54 | |
| 26 | С/у "М" | 5,74 | |
| 27 | С/узел | 3,11 | |
| 28 | Лестничная клетка | 15,56 | |
| 29 | Тамбур | 9,38 | |
| 30 | Тамбур - шлюз при кабинете для занятий музыкой | 2,07 | |
| Итого: | | | |