
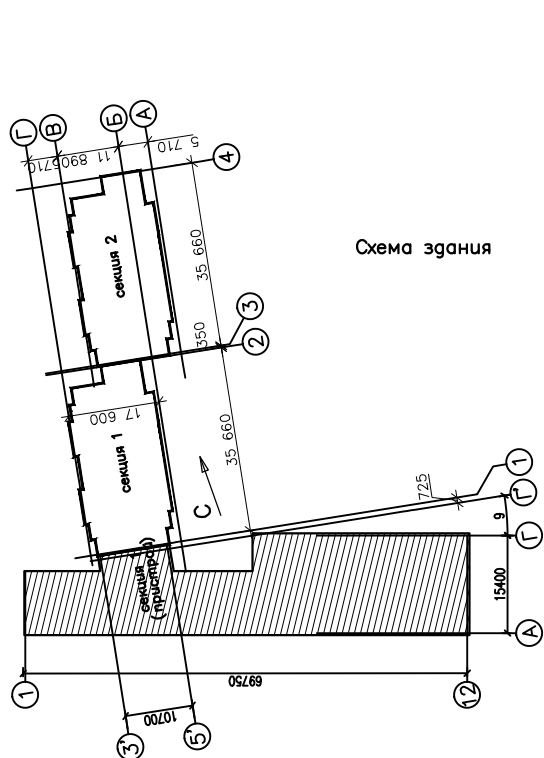


План 2-го этажа

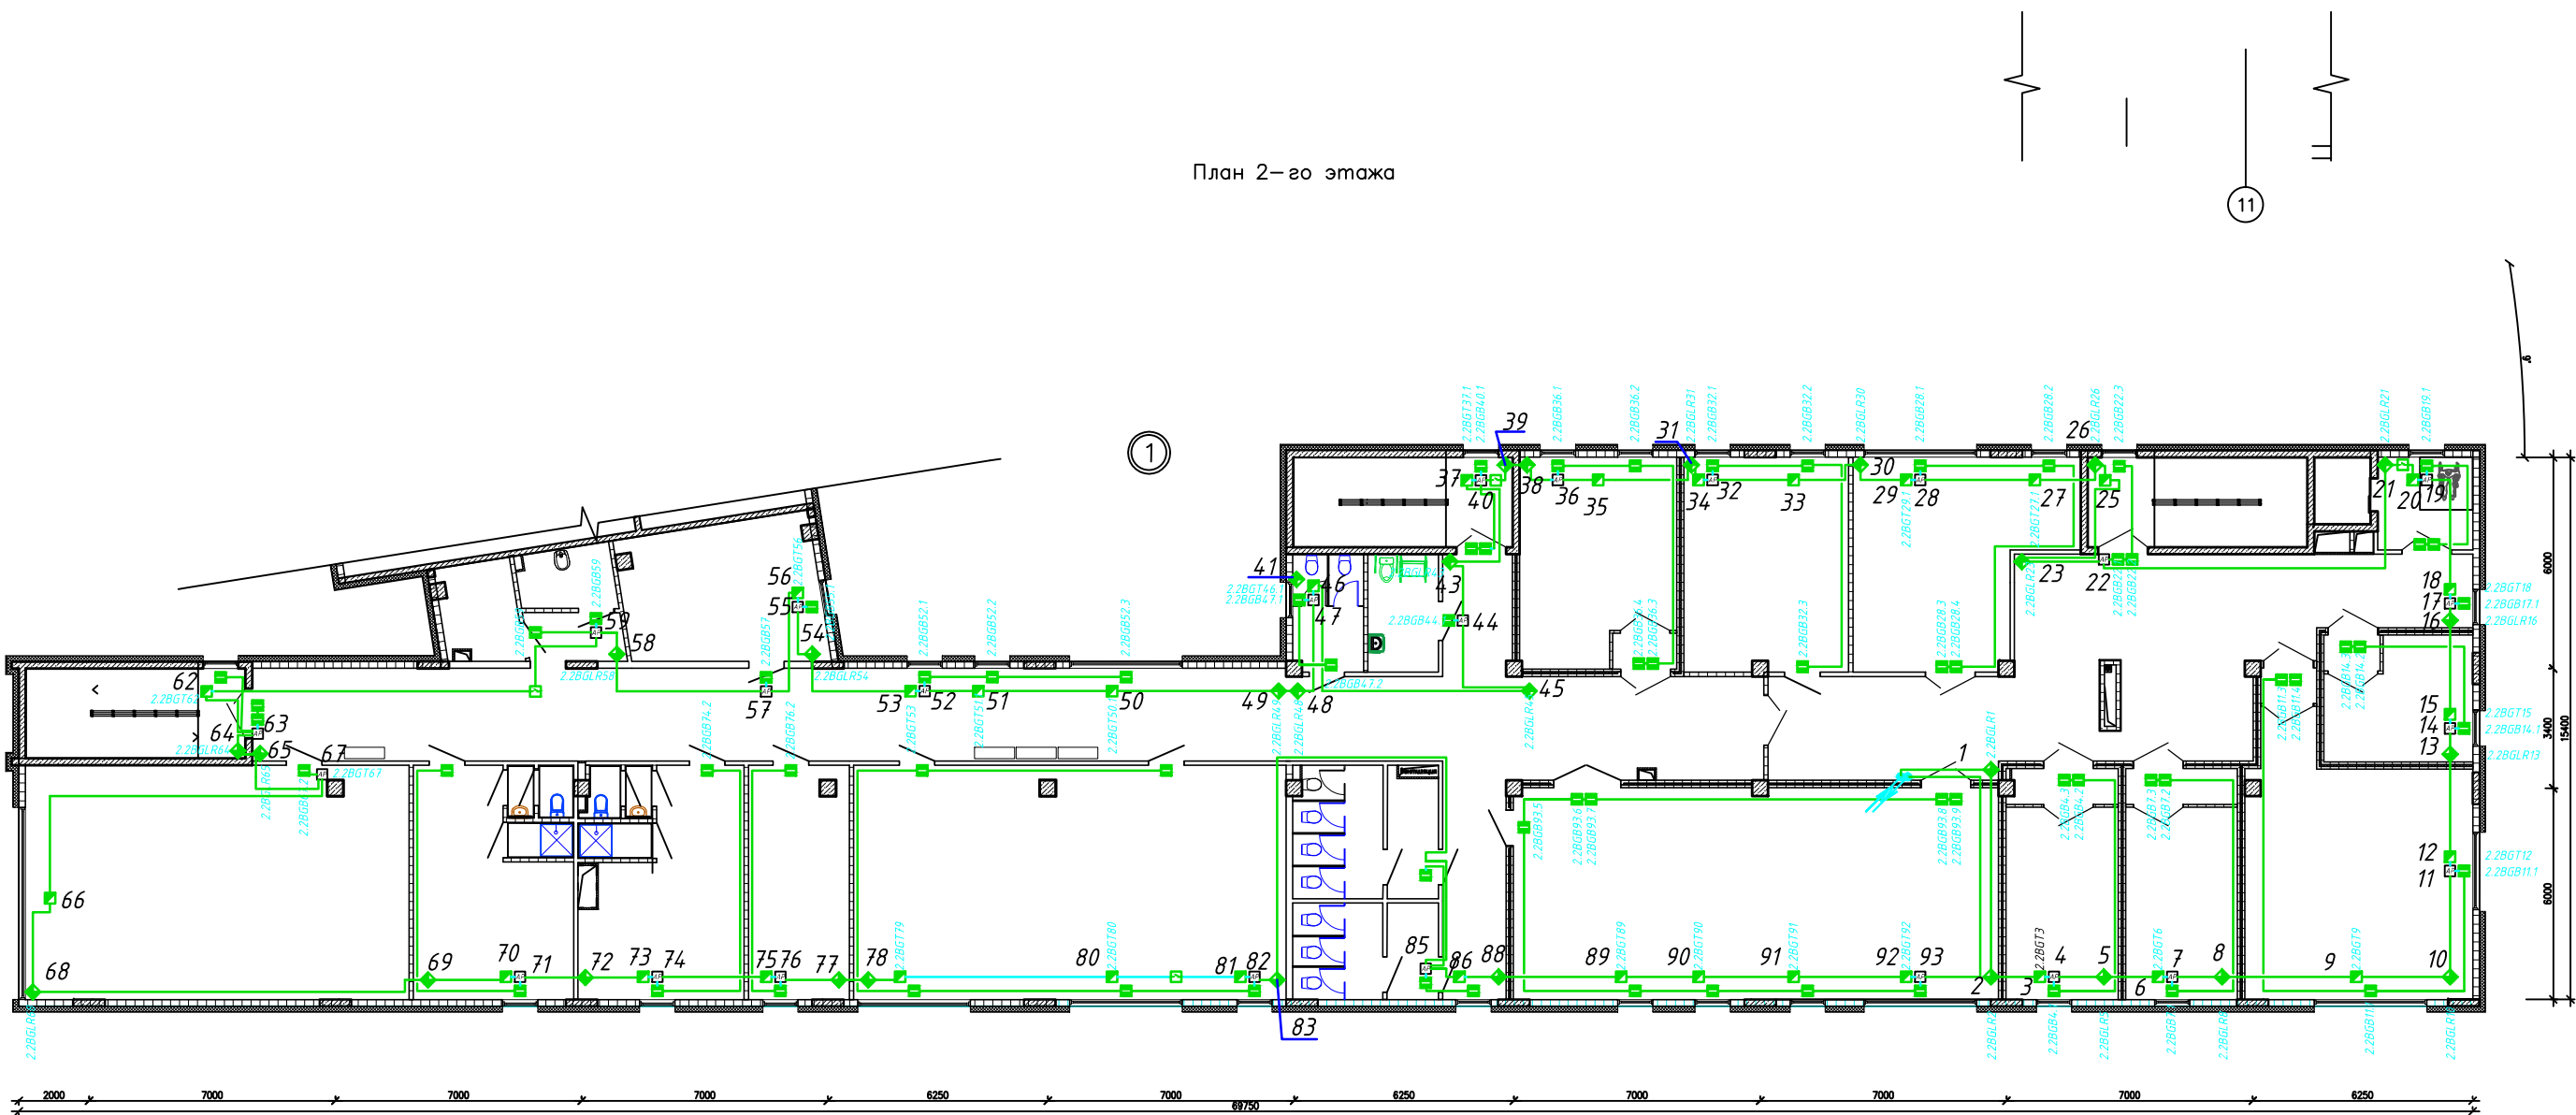

ЭКСПЛИКАЦИЯ ПОМЕЩЕНИЙ (начало)

Номер помещения	Наименование	Площадь, м2	Категория помещения
2 этаж Хореографическое и музыкальное отделение			
1	Лифтовой тамбур	7,13	
2	Лестничная клетка	15,56	
3	Коридор	72,85	
4	С/узел "Ж"	6,44	
5	С/узел "М", в том числе для МПН	6,46	
6	Класс групповых занятий (класс теоретических дисциплин) 16 чел. в группе	32,01	
7	Класс групповых занятий (класс теоретических дисциплин) 14 чел. в группе	28,02	
8	Класс индивидуальных занятий (класс фортепиано, синтезатора) 1 чел.	13,08	
9	Коридор	54,29	
10	Класс индивидуальных занятий (класс эстрадного и академического вокала) 1 чел.	17,02	
11	Класс индивидуальных занятий (класс скрипки и виолончели) 1 чел.	17,13	

ЭКСПЛИКАЦИЯ ПОМЕЩЕНИЙ (продолжение)

Номер помещения	Наименование	Площадь, м2	Категория помещения
2 этаж Хореографическое и музыкальное отделение			
Музыкальное отделение			
12	Класс для занятий хора 22 чел.	44,49	
13	Класс индивидуальных занятий (класс духовых и народных инструментов) 12 чел.	24,35	
14	Зал для проведения мероприятий. 101 посад. место	101,00	
Хореографическое отделение			
15	Зал хореографии. 26 чел.	80,88	
16	Раздевалка "Ж"	24,06	
17	Костюмерная	18,49	
18	Раздевалка "М"	24,40	
19	Зал хореографии. 24 чел.	71,66	
20	Административный кабинет (учебная часть)	21,38	
21	Комната личной гигиены - С/узел "Ж" (КПЛ - С/узел)	4,41	
22	Помещение уборочного инвентаря	5,65	В 4

ЭКСПЛИКАЦИЯ ПОМЕЩЕНИЙ (окончание)

Номер помещения	Наименование	Площадь, м2	Категория помещения
2 этаж Хореографическое и музыкальное отделение			
23	Коридор	80,33	
24	Лестничная клетка	15,56	
25	С/узел	4,90	
26	Душевые	3,20	
27	Лестничная клетка	15,56	
28	С/узел "Ж"	14,12	
29	С/узел "М"	10,65	
30	Тамбур - шлюзы при кабинетах для занятий музыкой		
Итого:			

01-21-ИОС.ОПС					
Перепланировка нежилого помещения, расположенного по адресу: г. Тюмень, ул. Западная, д. 9, для размещения детской школы искусств					
Изм.	Лист	Ндк.	Подпись	Дата	
Разраб.	Векшица	Богданов			
ГИП	Богданов				
Система автоматической охранной и тревожной сигнализации				Страница	Лист
				П	18
				Листов	
				ООО "РОСПРОЕКТ"	