



## План технopolья

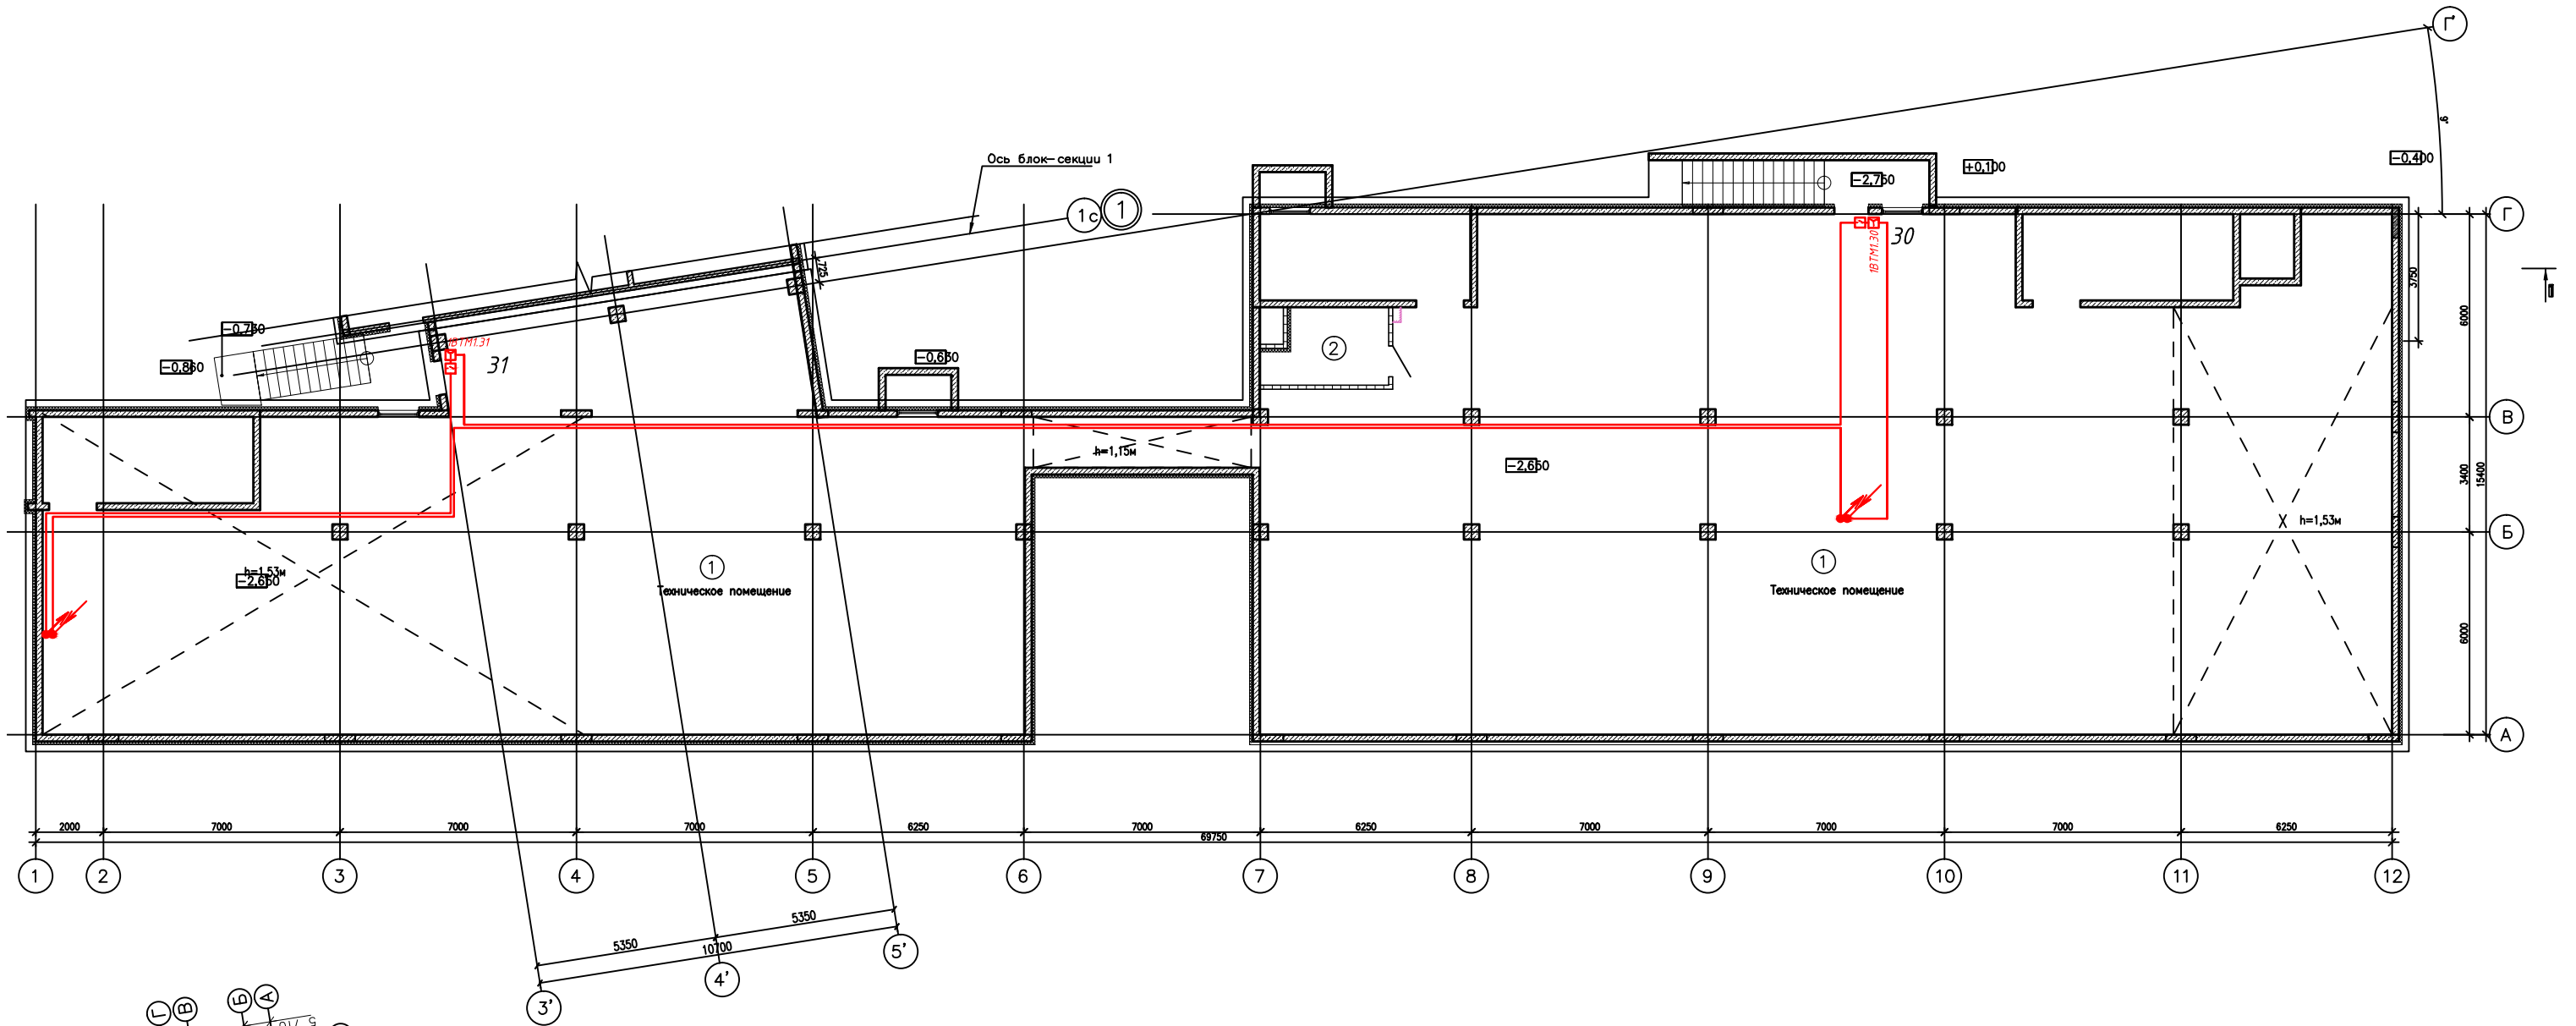

### Схема здания

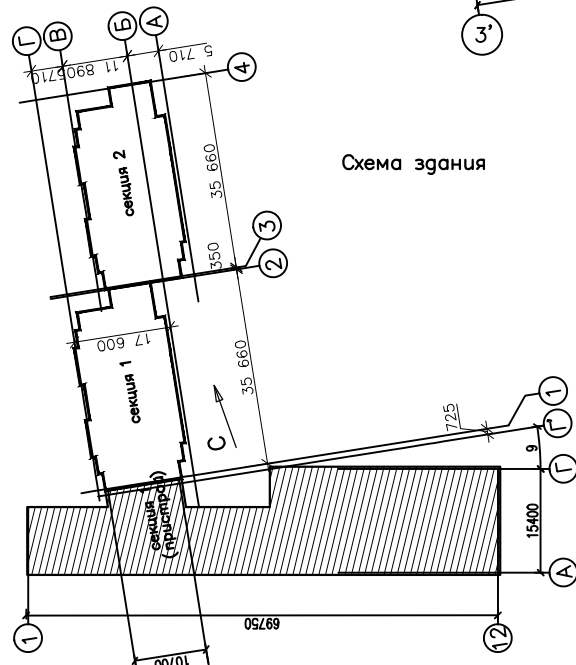

## ЭКСПЛИКАЦИЯ ПОМЕЩЕНИЙ

Номер помещения	Наименование	Площадь м2	Категория помещения
Техпоглолье			
1	Техническое помещение	818,53	
2	Венткамера	7,37	Д

						01-21-ИОС.ОПС					
						Перепланировка нежилого помещения, расположенного по адресу: г.Тюмень, ул.Запольная, д.9, для размещения детской школы искусств					
Изм.	Нач.	Лист	Ндок.	Подпись			Дата				
Разраб.	Вешкиричева	Вешкирева									