

План техногопол


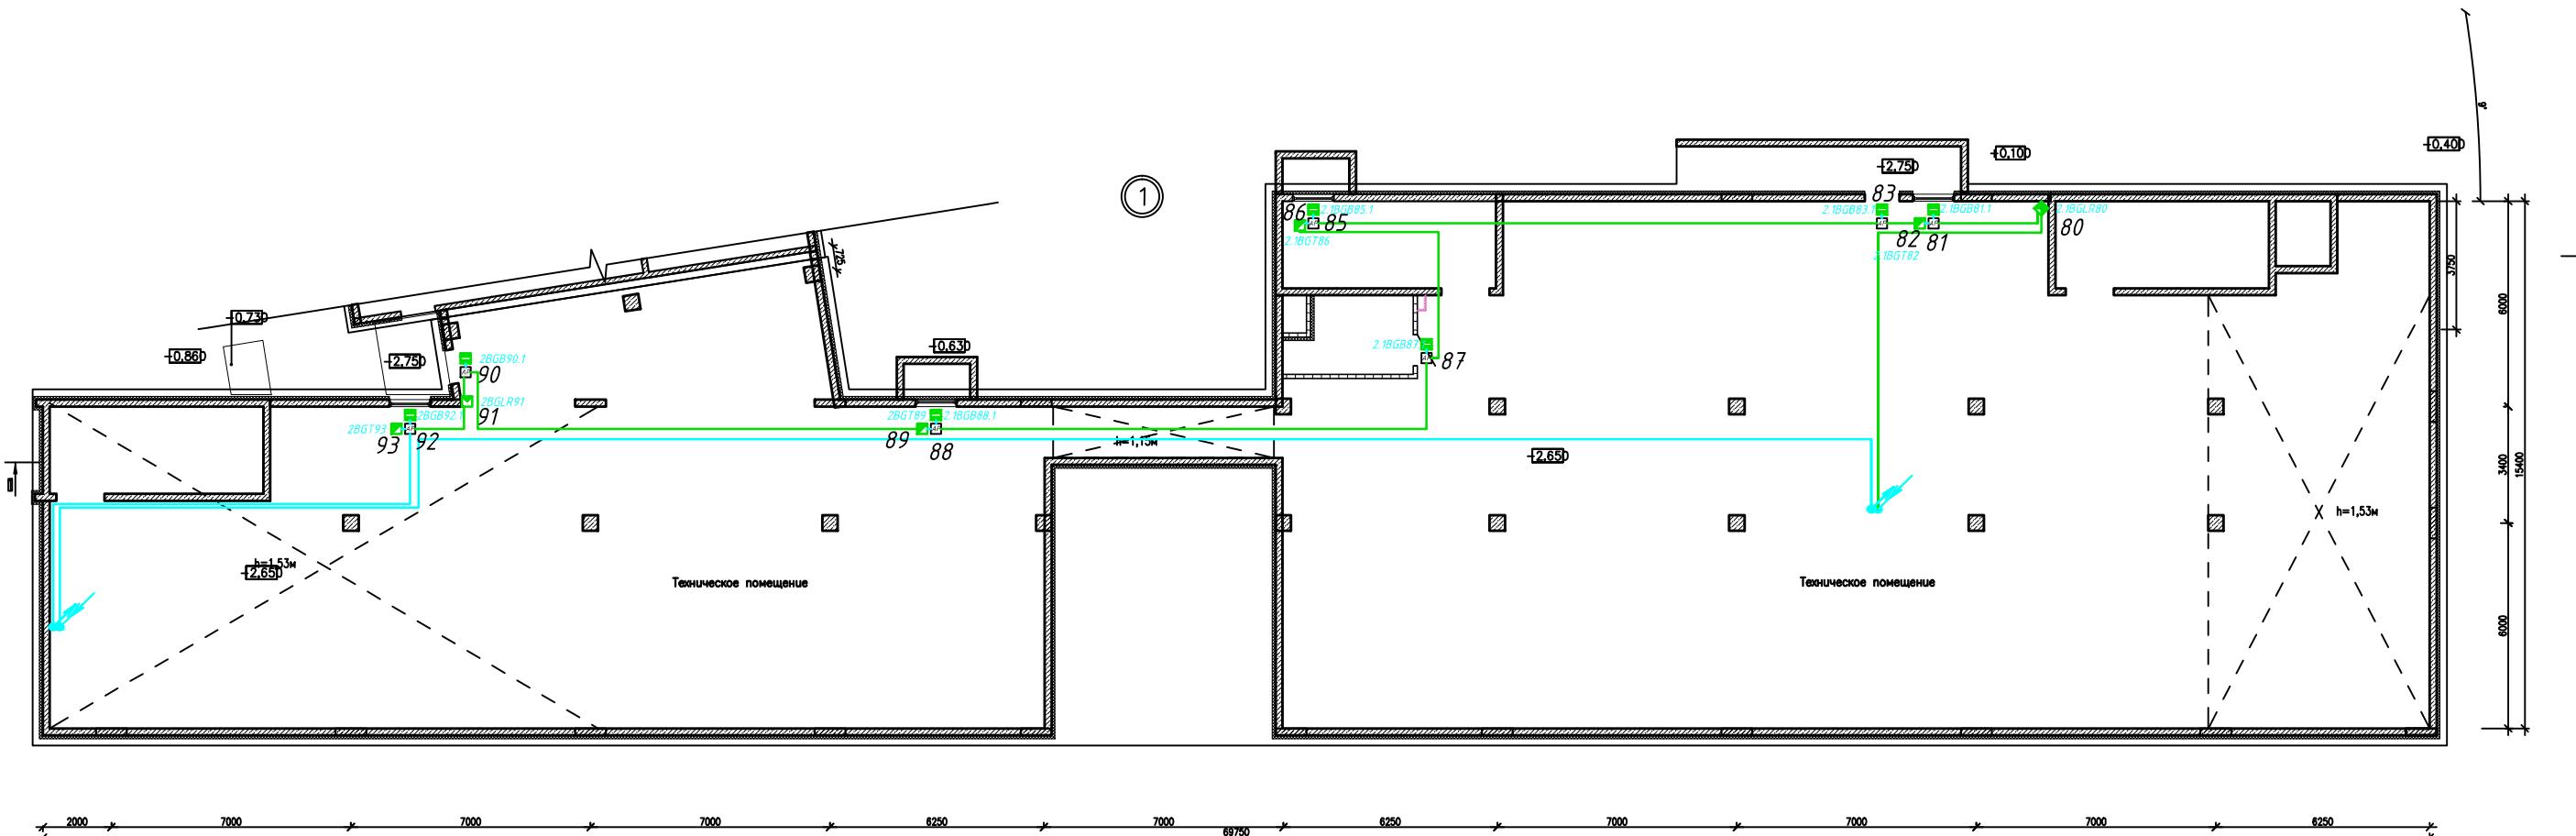


Схема зданн

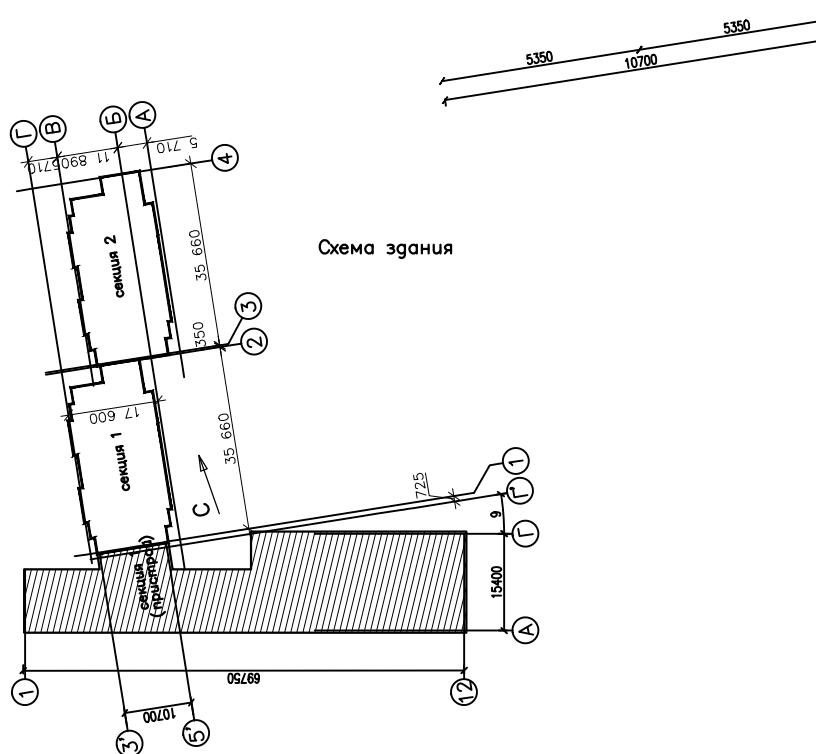

ЭКСПЛИКАЦИЯ ПОМЕЩЕНИЙ

Номер помещения	Наименование	Площадь м ²	Капиталоемкость
Теплополье			
1	Техническое помещение	818,53	
2	Венткамера	7,37	

21-21-K25-276

Перепланировка нежилого помещения, расположенного по адресу: г. Тюмень, ул. Заполярная, д. 9, для размещения детской школы искусств № 8

Изм	Нуч	Лист	№док.	Подпись
Разрд.	Вешкүрцева	Беким		
ГИП	Богданов			

Система автоматической
охранной и тревожной сигнализации
ООО "РОСТПРОЕКТ"